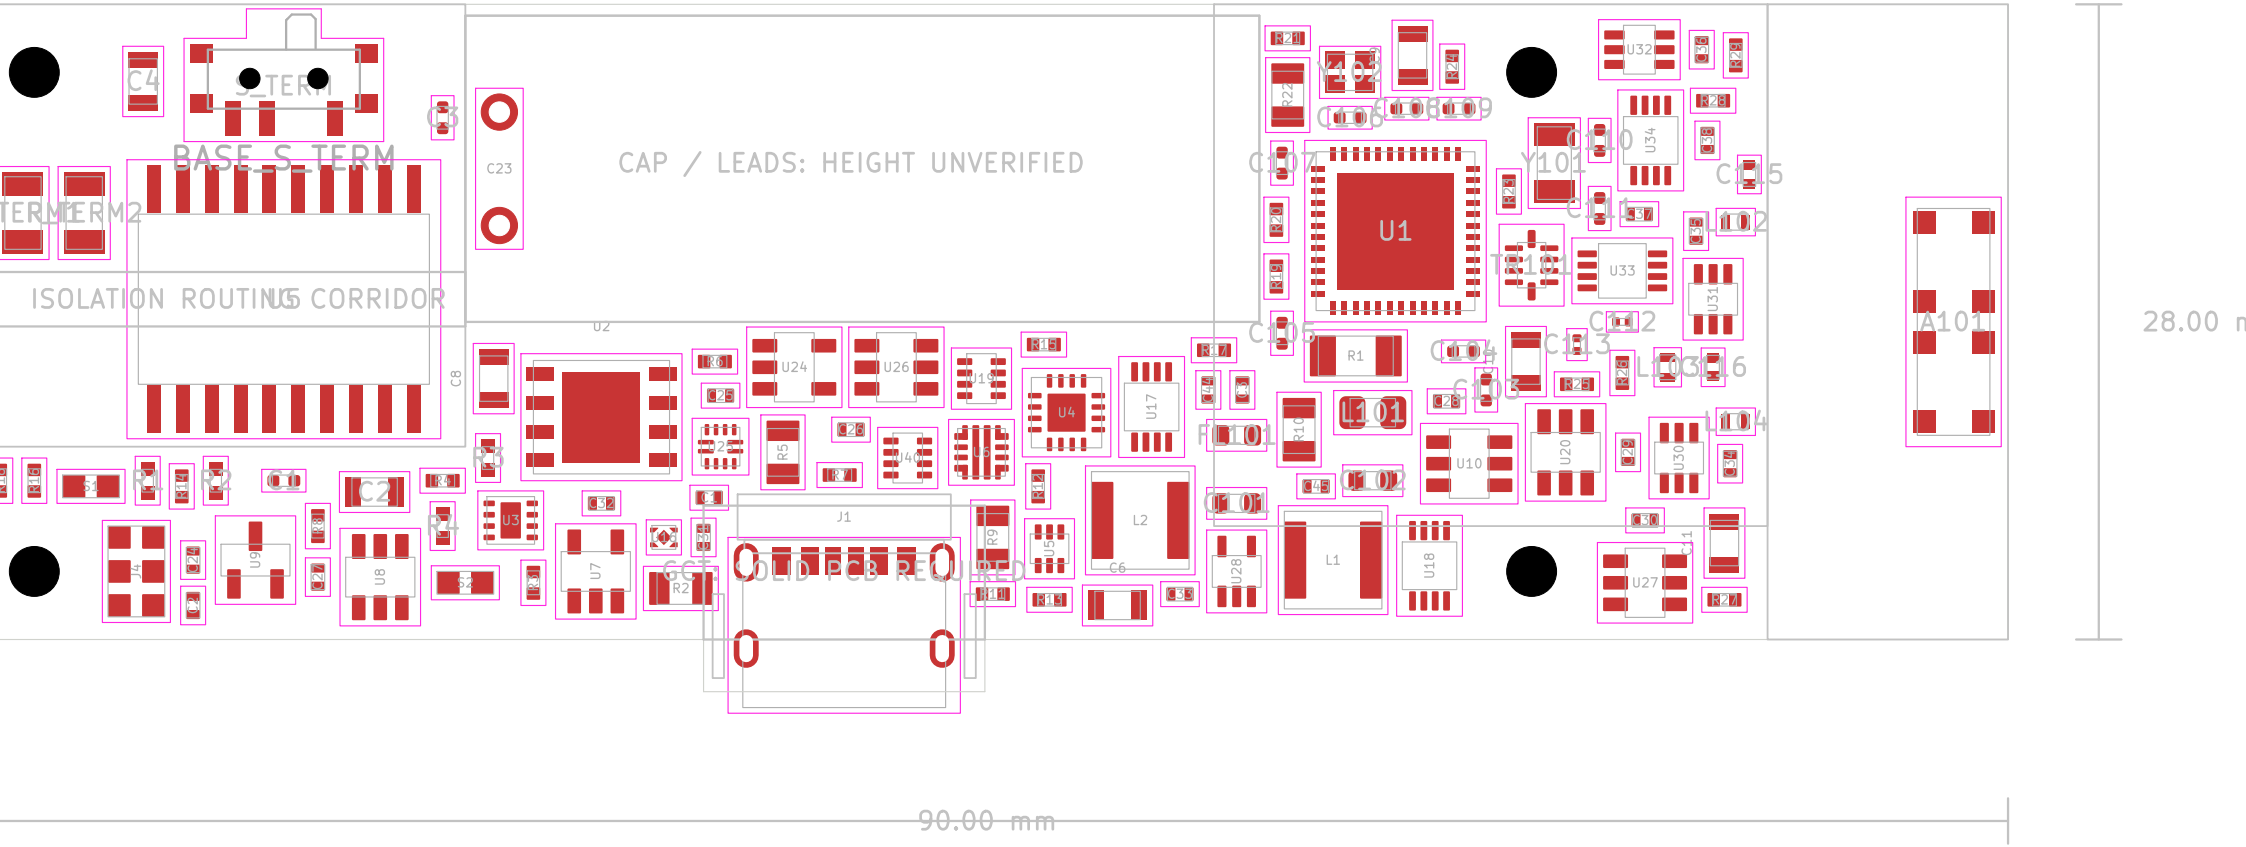

S_TERM
BASE_S_TERM
TERM1
TERM2
ISOLATION ROUTING CORRIDOR
CAP / LEADS: HEIGHT UNVERIFIED
SOLID PCB REQUIRED
U1
A101
28.00 mm
90.00 mm